РАСКРОЙ ТРУБ РАМЫ 20×20×2 — 4 ТРУБЫ ПО 1000 мм

fix11 · сварная рама, 18 отрезков · рез ≤5 мм · масштаб 1:5

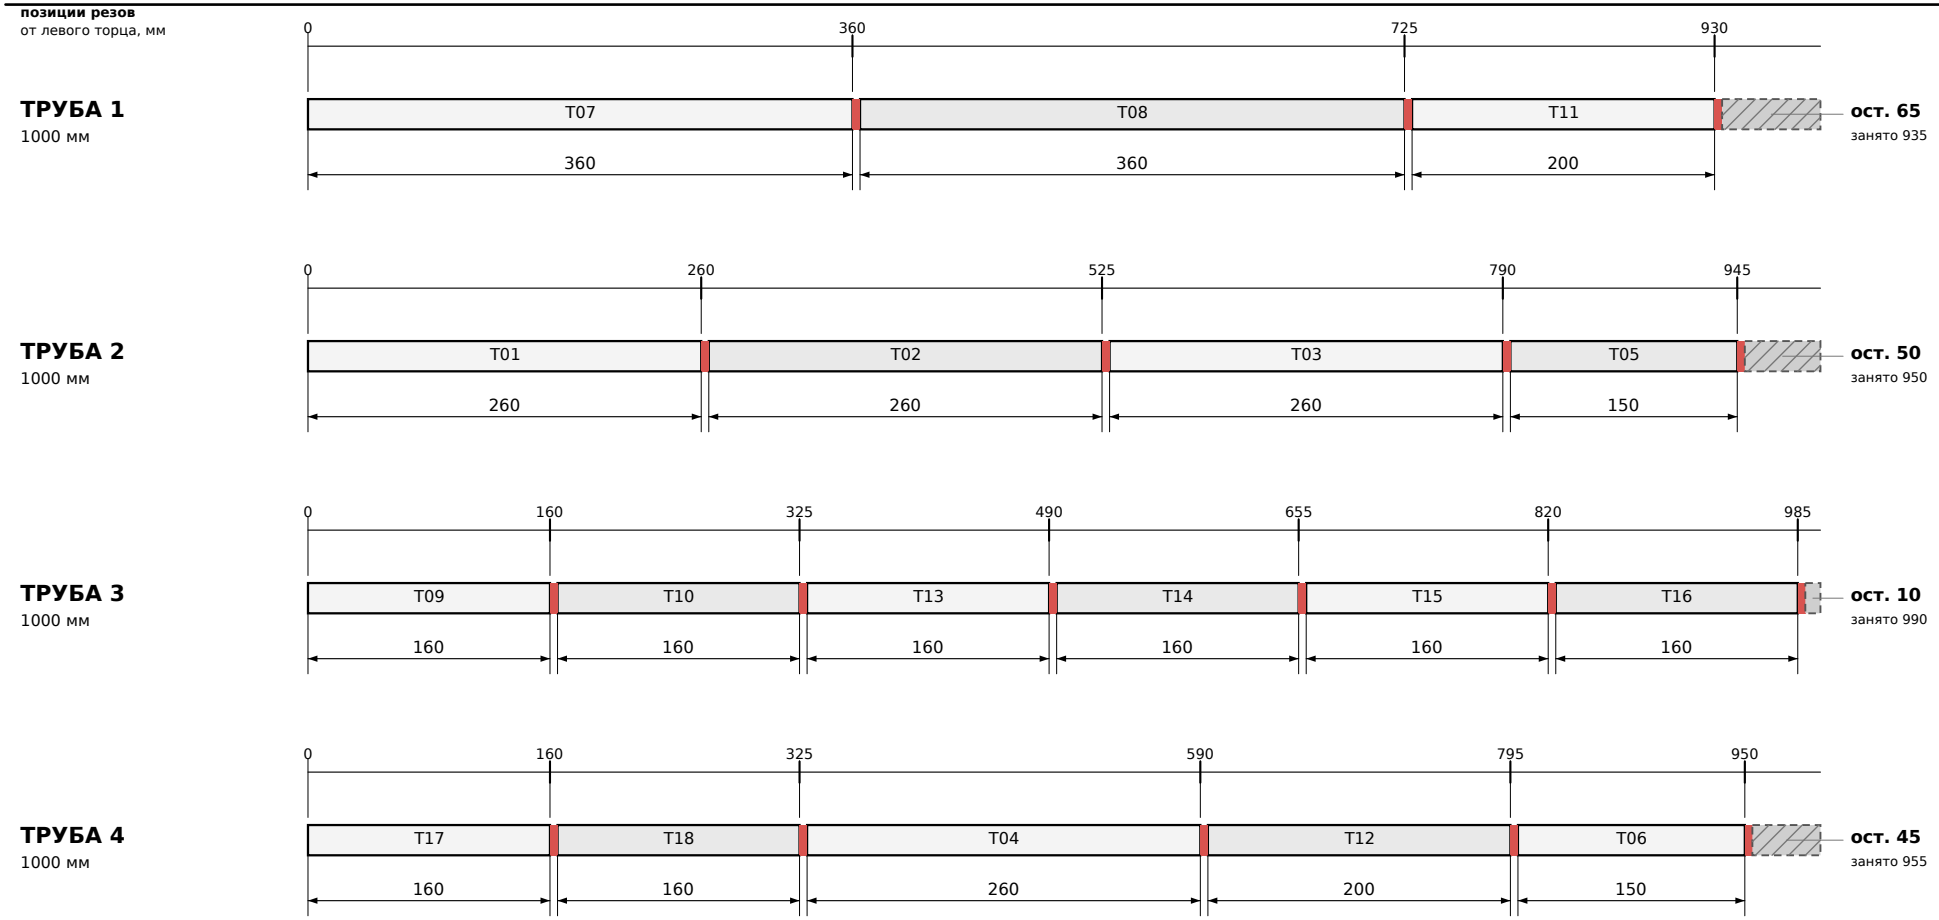

ПРИМЕЧАНИЯ

1. Сталь 20×20×2; 4 трубы по 1000 мм. Размеры — готовые длины, рез 5 мм учтён; при меньшем резе остатки растут. 3740 + 18×5 = 3830; остаток 170 мм.
2. Резать по длинам; позиции — для реза 5 мм; резы 90°, заусенцы снять.
3. Отверстия/прорези — по листам 22_T01…T18: T13/T14 — Ø10 верх. стенка; T17/T18 — прорезь R15.
4. Поджимные балки 21 (2×159,6) — из отдельной трубы.
5. Масштаб 1:5; деталь А — 1:1.

Тр.	Позиции	Длины, мм	Резы от торца, мм	Ост.
1	T07 T08 T11	360+360+200	360·725·930	65
2	T01 T02 T03 T05	260+260+260+150	260·525·790·945	50
3	T09 T10 T13 T14 T15 T16	160+160+160+160+160+160	160·325·490·655·820·985	10
4	T17 T18 T04 T12 T06	160+160+260+200+150	160·325·590·795·950	45
Итого	**18 отрезков**	**3740**	**рез 90**	**170**

ДЕТАЛЬ А — РЕЗ ≤5 мм (1:1)

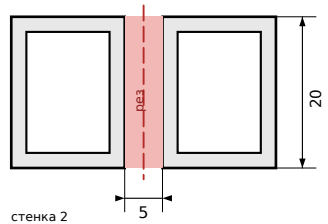

fix11 · РАСКРОЙ ТРУБ РАМЫ сталь 20×20×2 · 4 трубы × 1000 мм · рез ≤5 мм	МАСШТАБ **1:5**	ЛИСТ **1/1**	РЕЗ **≤5 мм**	ДАТА 04.11.2026	РАЗРАБОТАЛ DeepSeek / OpenCode